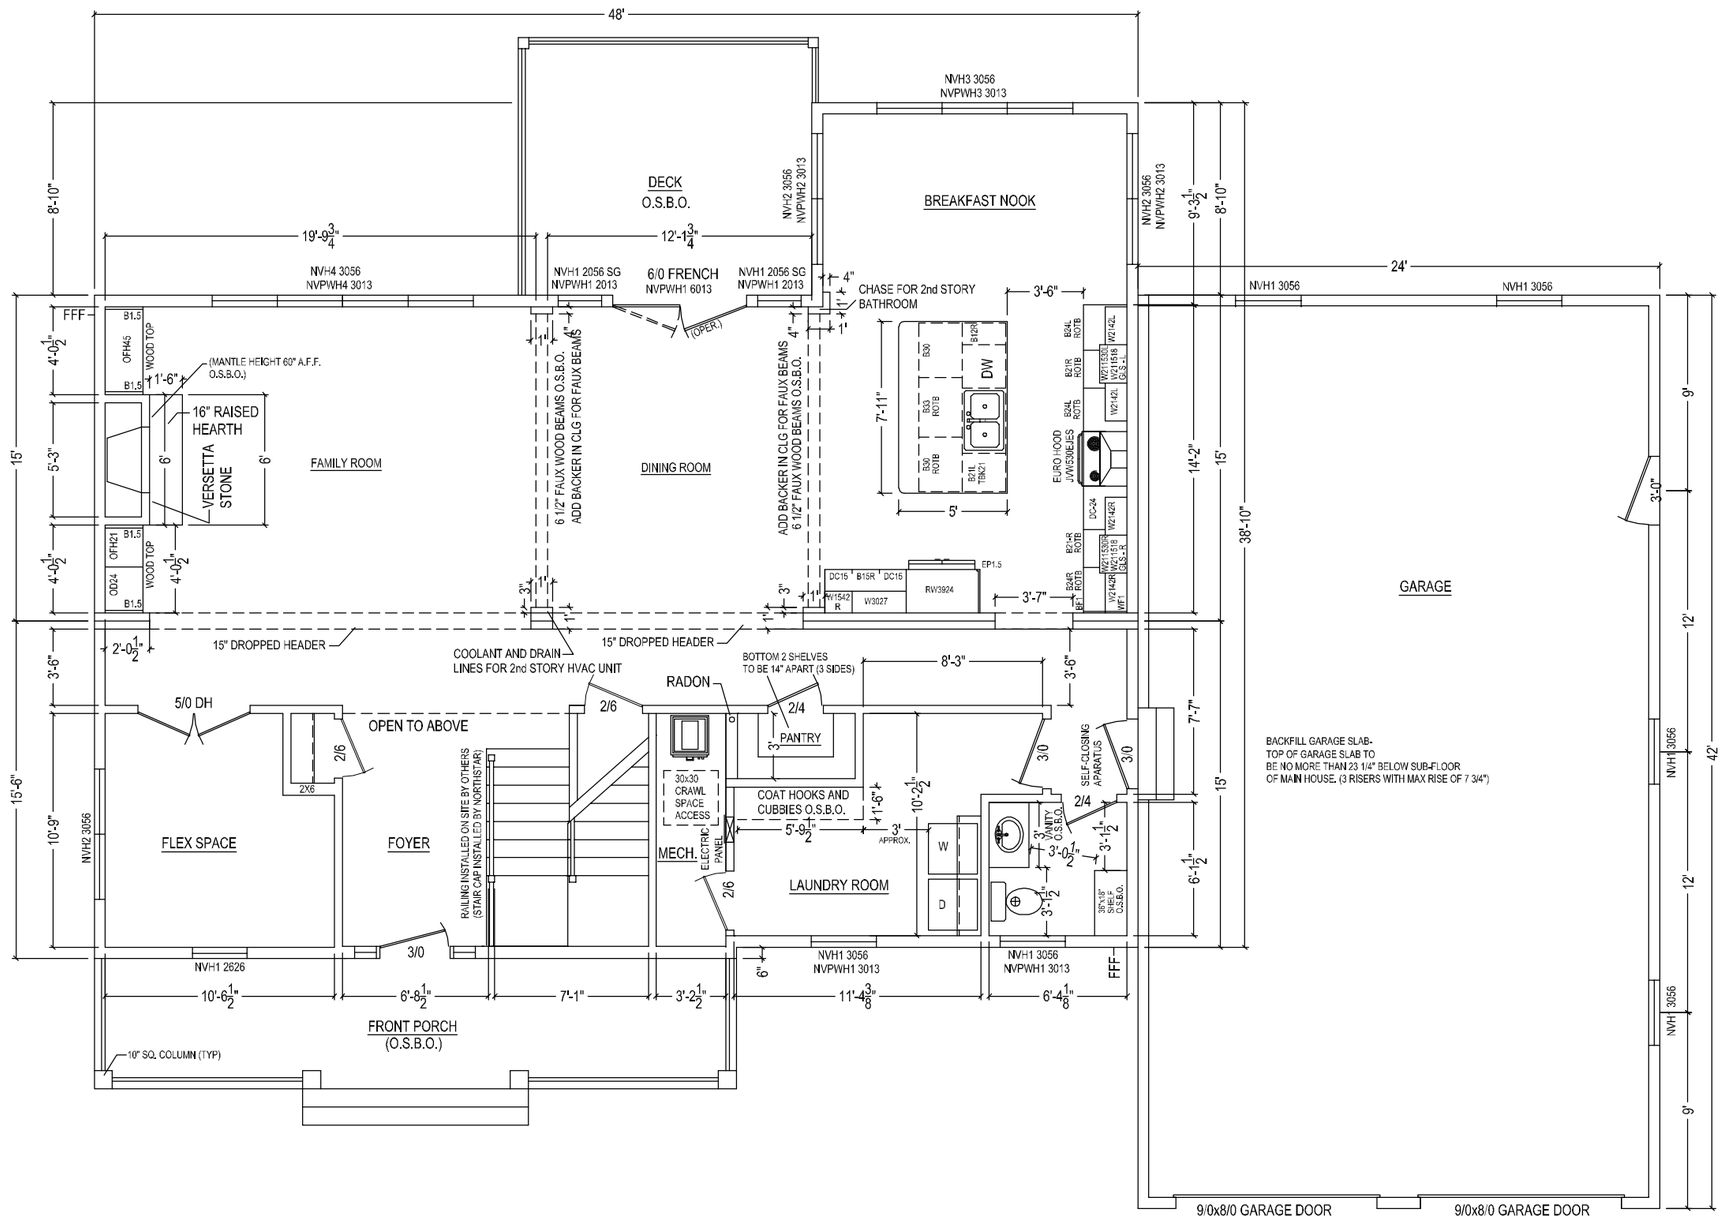

GARAGE BUILT ON SITE BY OTHERS. WINDOW AND GARAGE DOOR PLACEMENT MAY VARY.

ALL SINKS OMITTED (O.S.B.O.)
10' CEILINGS
ALL FLOORING ON SITE BY OTHERS
COUNTERTOPS ON SITE BY OTHERS- ROUGH PLUMBING STUBBED FOR ALL FIXTURES

NORTHSTAR SYSTEMBUILT
203 Industrial Drive
Redwood Falls, MN
Ph: (507) 644-6600
Fx: (507) 644-6601

1st LEVEL FLOOR PLAN

NS1619 (STEPHENSON)

DATE: 1-12-2017 | REV: A (4-20-2017) | DRAWN BY: KWL

PAGE: A1.0